


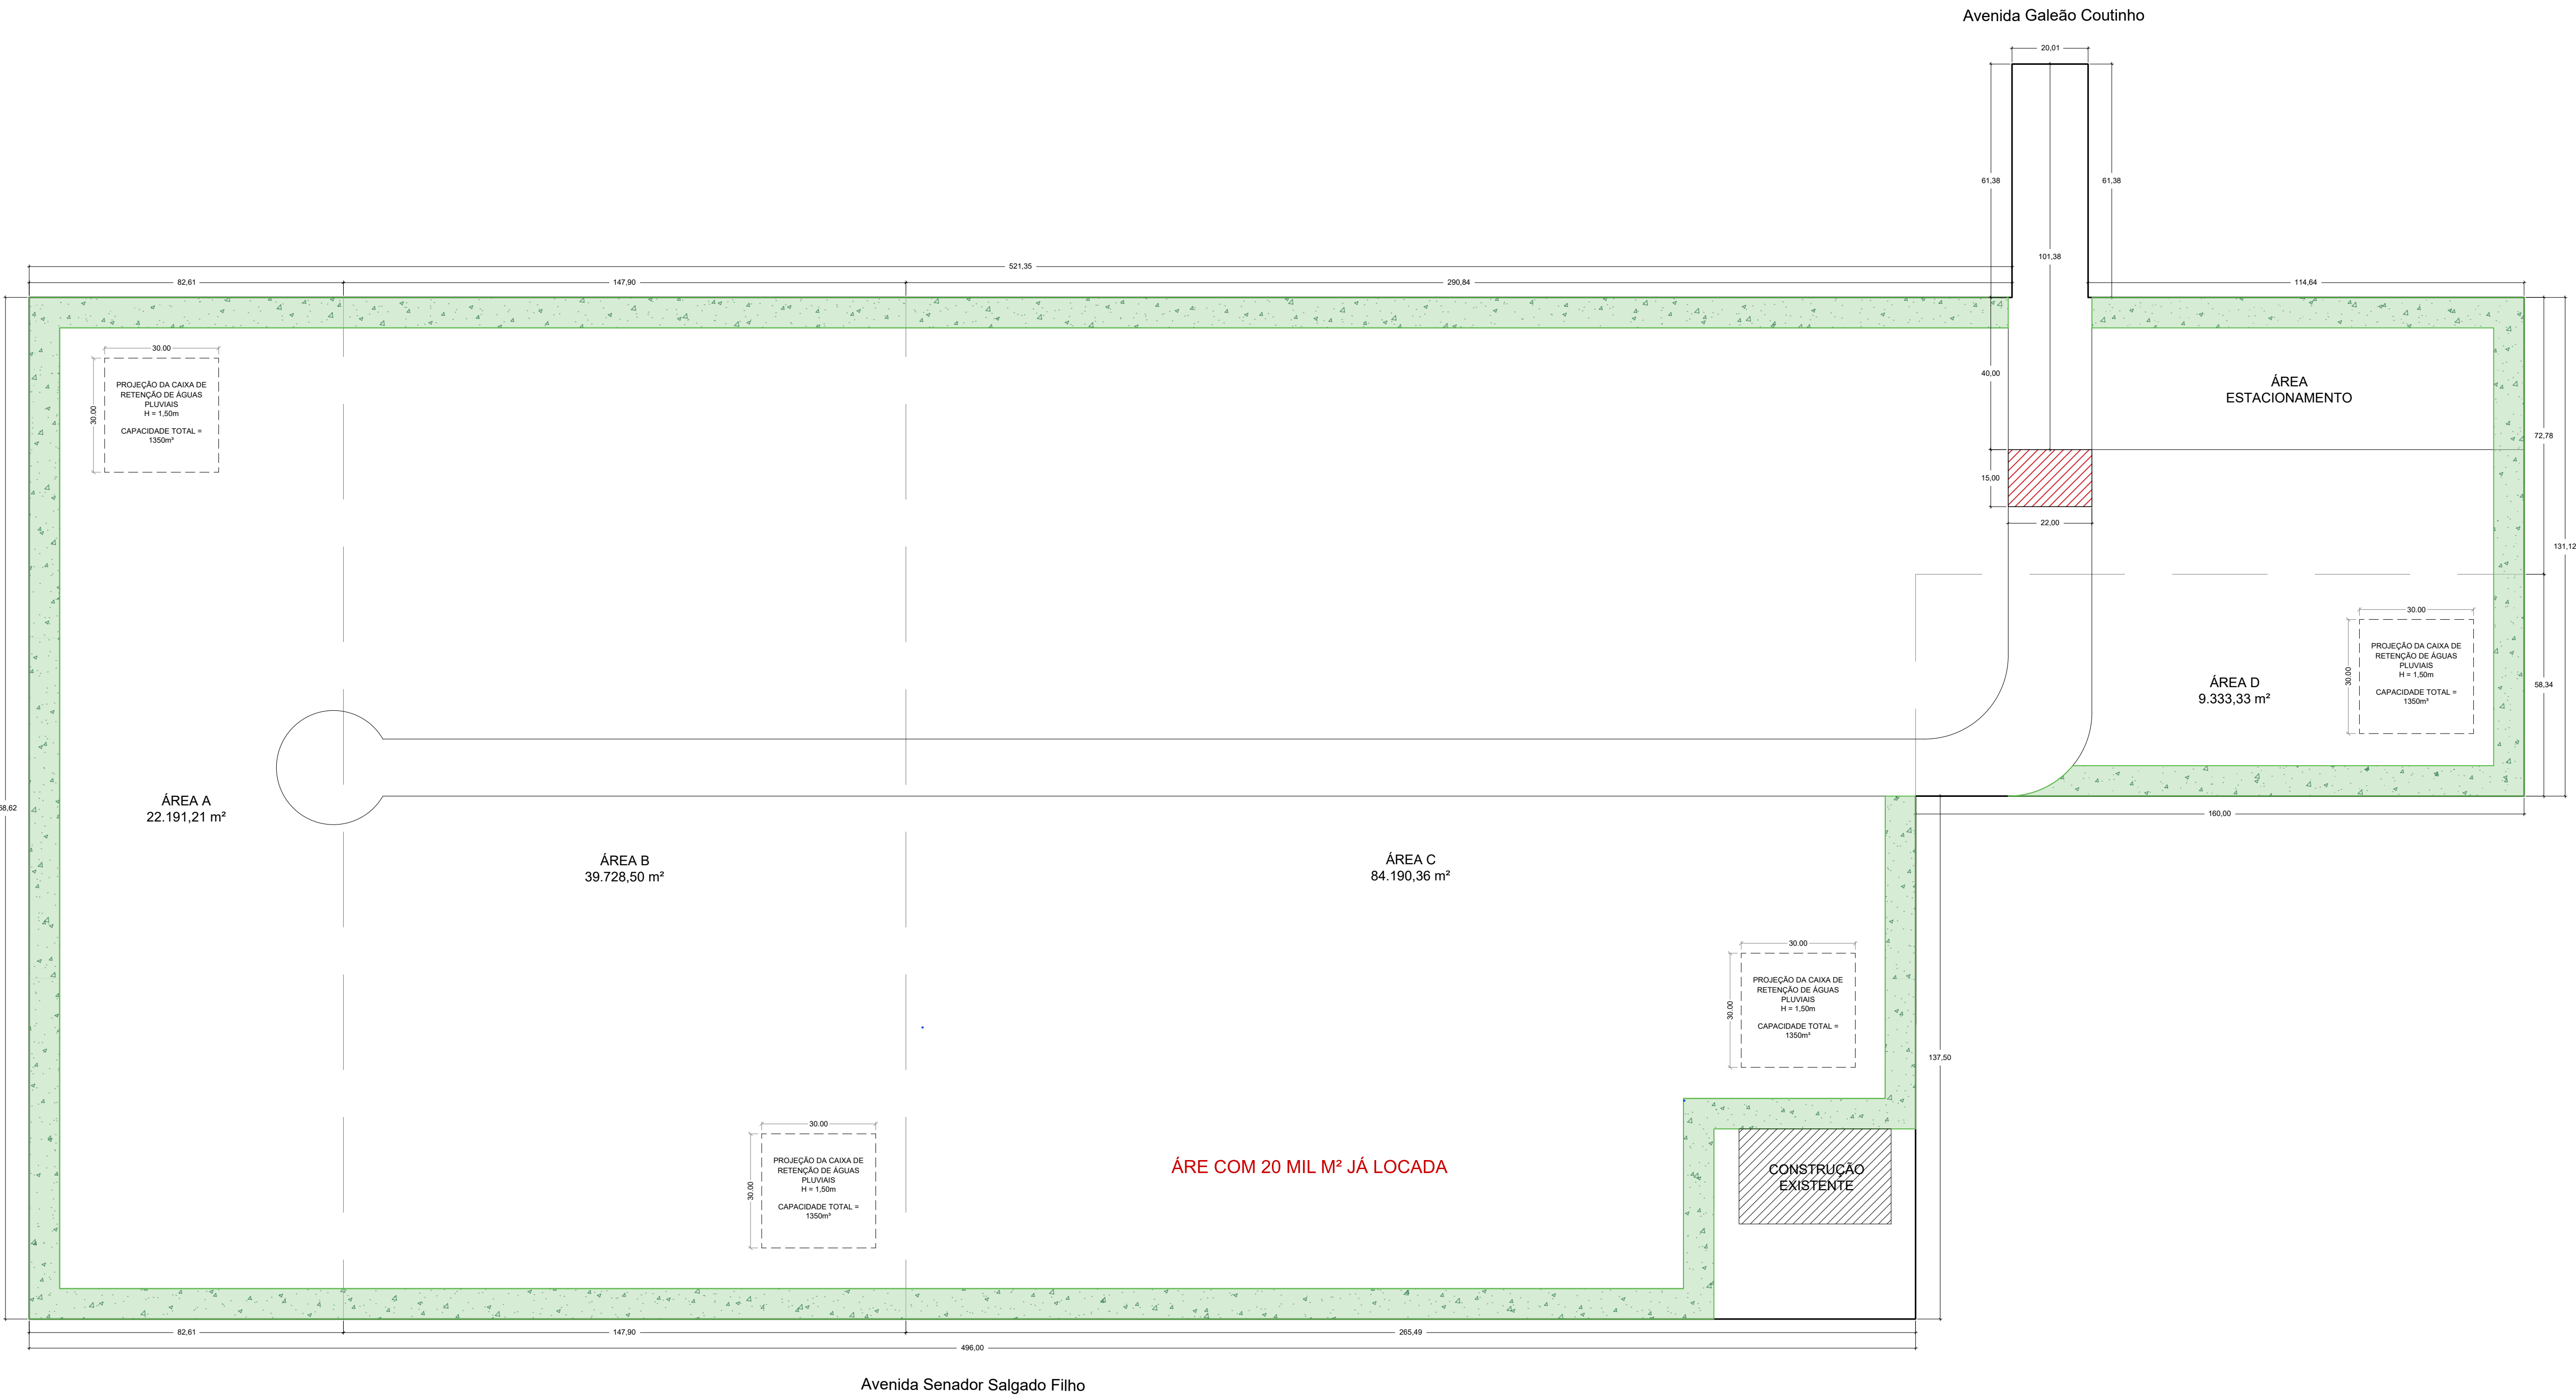

IMPLANTAÇÃO
ESCALA 1:1000

LEGENDA

EXISTENTE APROVADO
PROCESSO 4785/1956
ÁREA 243,40m²

ÁREA PERMEÁVEL

A CONSTRUIR

PROJETO ARQUITETÔNICO

ESCALA 1:100

FOLHA
01/02

TÍTULO: APROVAÇÃO DE PROJETO DE CONSTRUÇÃO DE TERMINAL LOGÍSTICO

LOCAL: Avenida Galeão Coutinho, Avenida Senador Salgado Filho e Rua Duarte da Costa
Vila Jóquei Clube - São Vicente

PROPRIETÁRIO: TMK ENGENHARIA S.A.

SITUAÇÃO S/ ESCALA

Declaro que a aprovação do projeto não implica no reconhecimento por parte da prefeitura no direito de propriedade do terreno.

ÁREAS EM m²

ÁREA A	22.191,21
ÁREA B	39.728,50
ÁREA C	84.190,36
ÁREA D	9.333,33

À CONSTRUIR

PAVIMENTO TÉRREO	330,00
PRIMEIRO PAVIMENTO	96,75
SEGUNDO PAVIMENTO	330,00
TOTAL À CONSTRUIR	756,75
Á. PERMEÁVEL	14.007,72

TMK ENGENHARIA S.A.
CNPJ: 28.131.759/0001-22
PROPRIETÁRIO

AUTOR DO PROJETO E RESP. TÉCNICO
RAPHAEL GOMES M. SORIANO DE OLIVEIRA
ARQUITETO E URBANISTA
CAU A 63792-0