



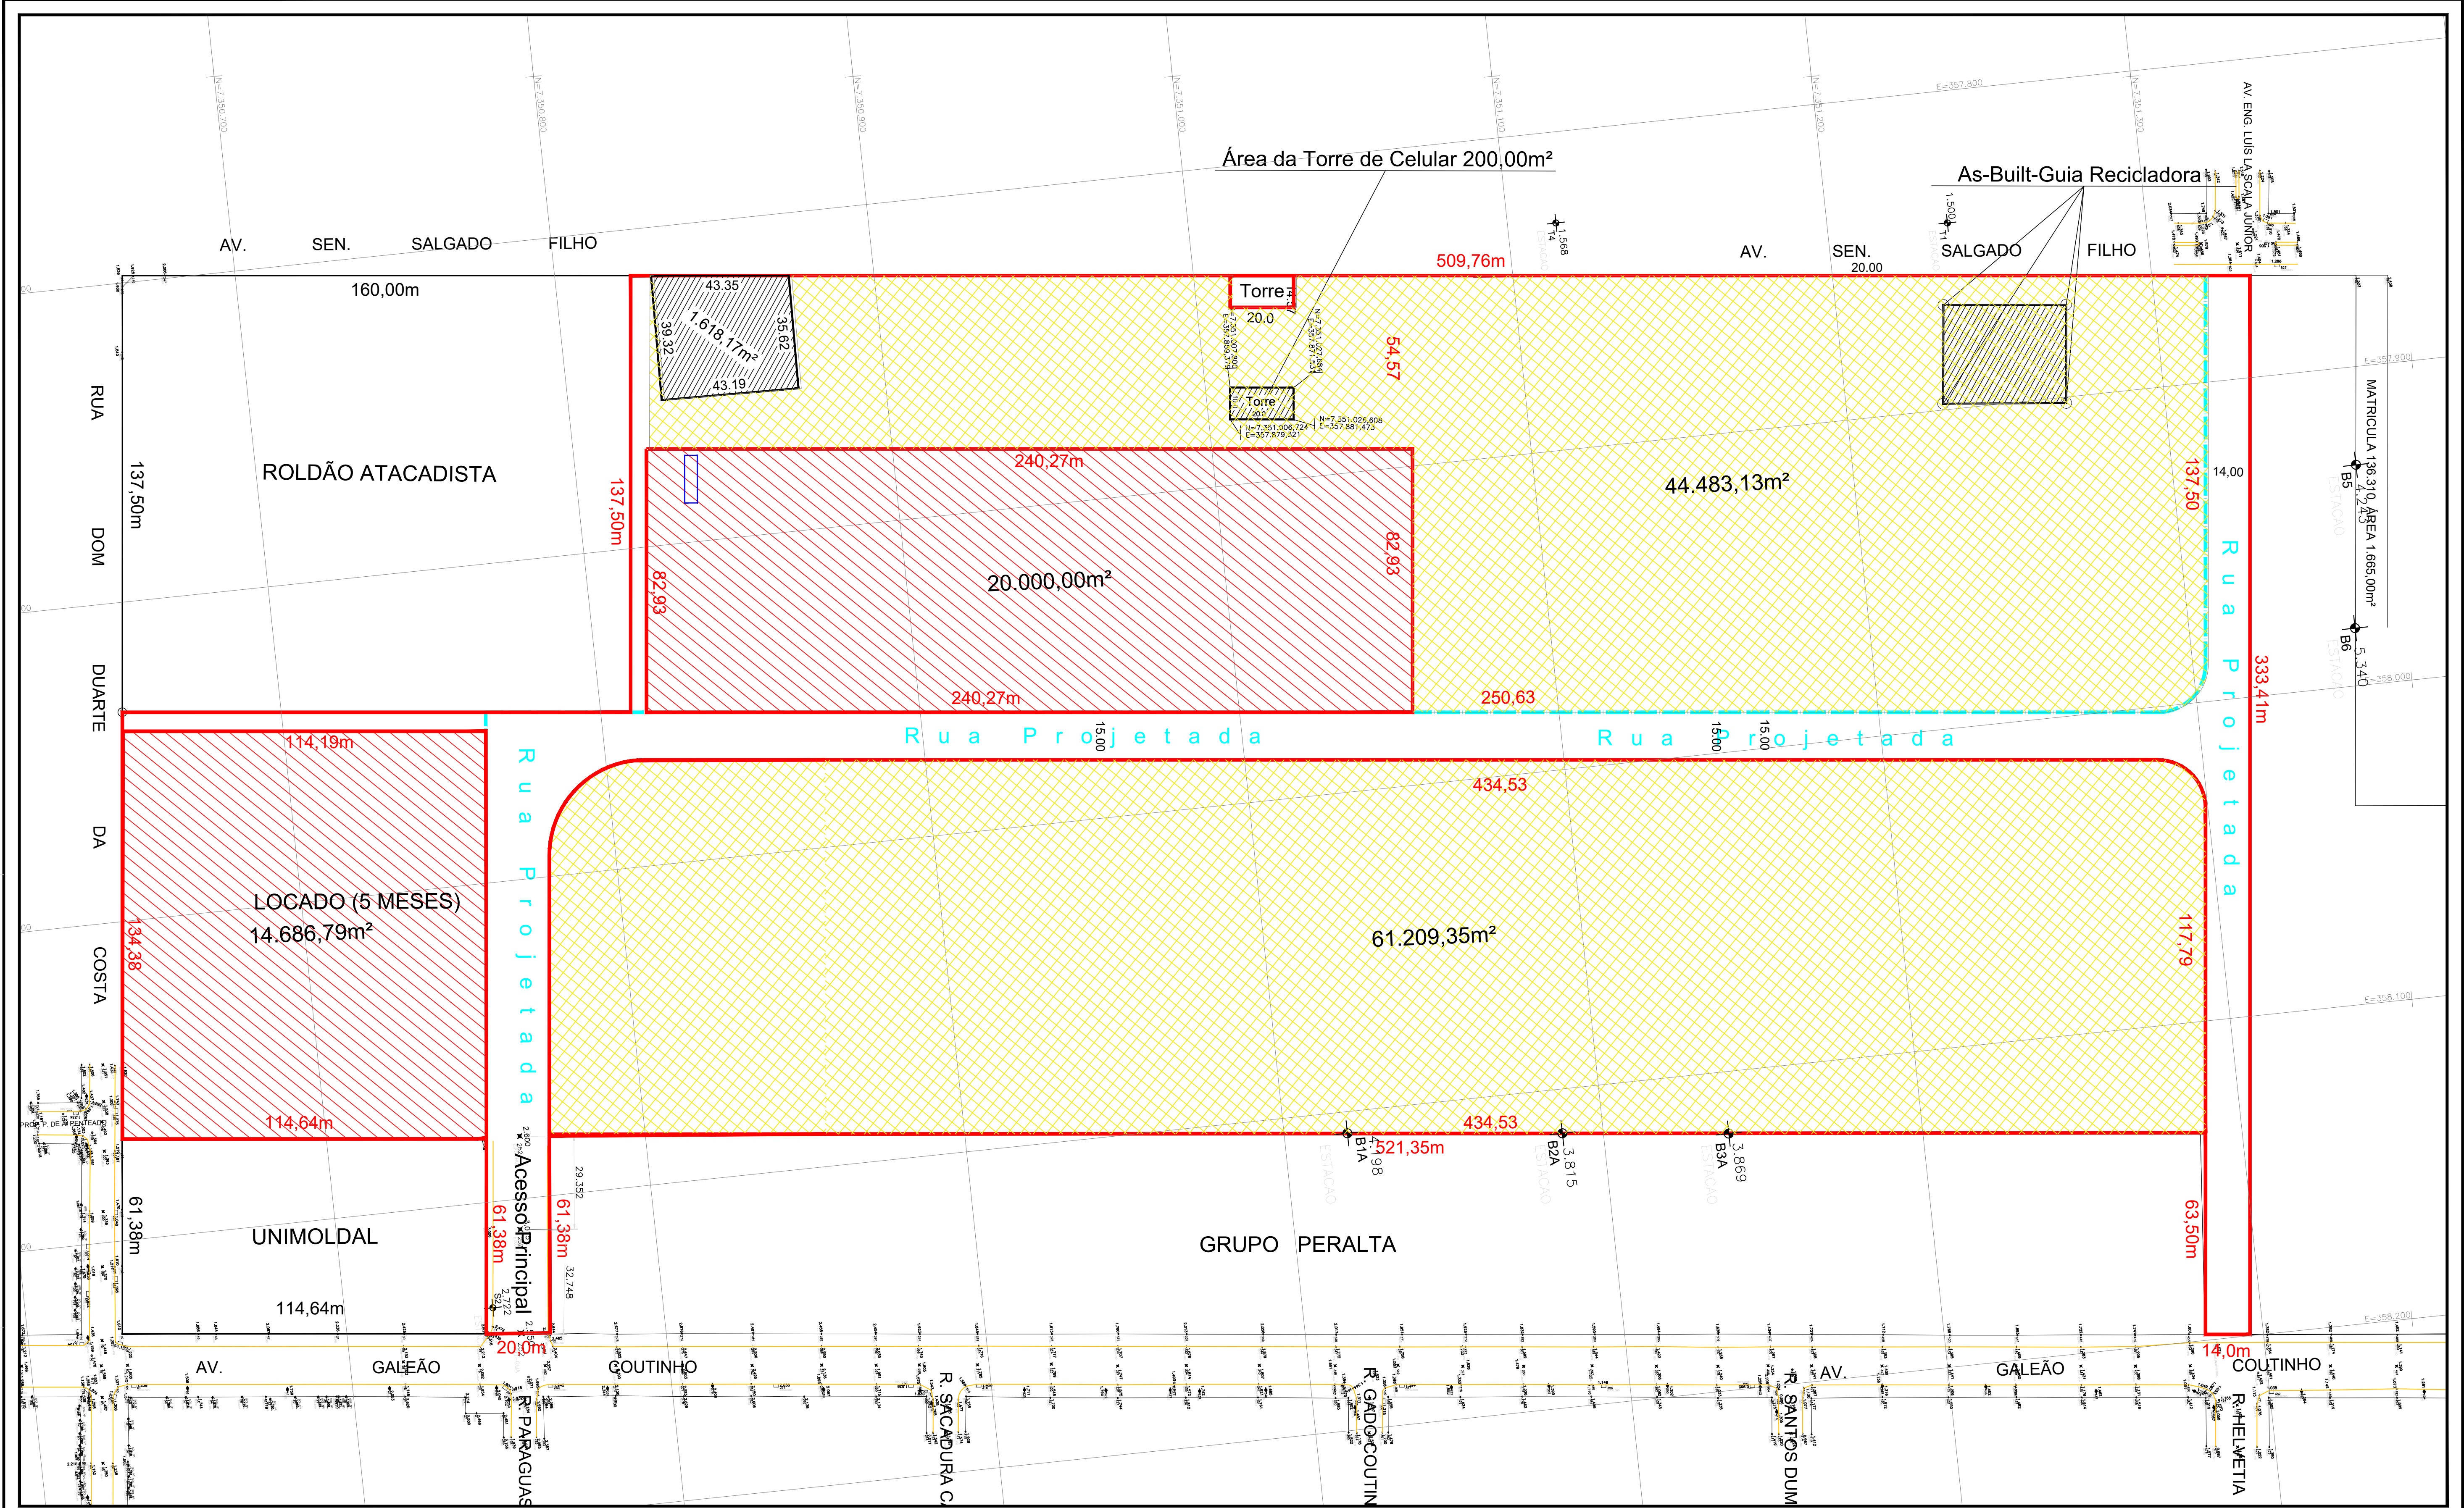

Observações:

Lev. Top. Planialt. e Cad., Feito com RTK (Sirgas 2000) Ajustado Pelo Ponto da Base (S1), para Coordenadas Topográfica Local.

Os Limites das Matrículas Foram ajustadas para os respectivos Muros Existentes no Local, principalmente na Divisa do Grupo Peralta a da Unimoldal.

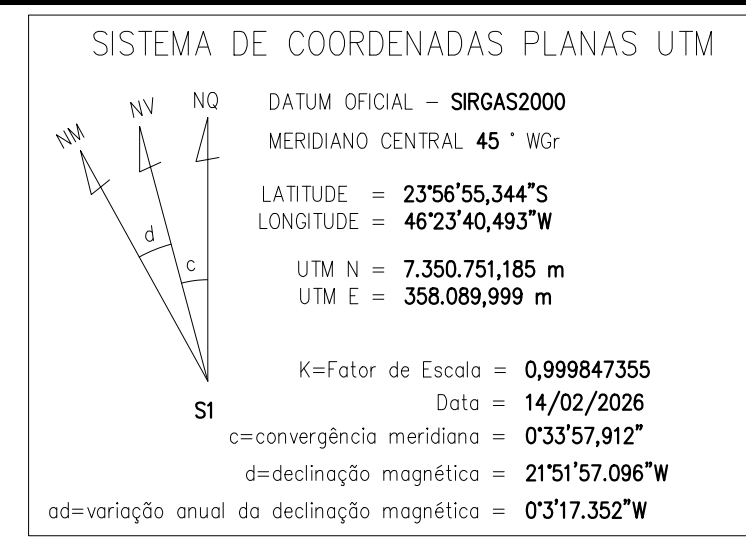

- Legenda:
- Linha de Guia Existente
 - Perímetro da Área
 - Limite de Rua Projetada
 - Muro ou Predial Existente
 - Polig. de Apoio ou Amarrações
 - Cota de Terrap. Acab. (Interna)
 - Poço de Vista A. Pluviais
 - Poço de Vista Esgoto
 - Boca de Lobo ou Grelha
 - Poste de Energia
 - Soleira Residencial
 - Indicação de Fluxo Pluvial
 - Área Locada
 - Área Livre

TMK - Engenharia Ltda.				
TÍTULO:		Projeto Interno de Terraplanagem (Cotas de Acabamento).		
DESCRIÇÃO:		Levant.Top., Planimétrico, Georreferenciado		
LOCAL:		Av. Galeão Coutinho, nº 513B - Bairro Jockey Clube - São Vicente - SP.		
ENGº RESP.:	Fernando Borges	COORD. TÉCN.:	Wellington P. Silva	ESCALA: 1 / 750
ARQUIVO:	PROJ_INTERNO_TERRAP-06	TOPOGRAFO:	Vinicius Leite	FOLHA: 01-01
		DATA :	13/07/2026	REV: 06